

CASA DE HABITACION

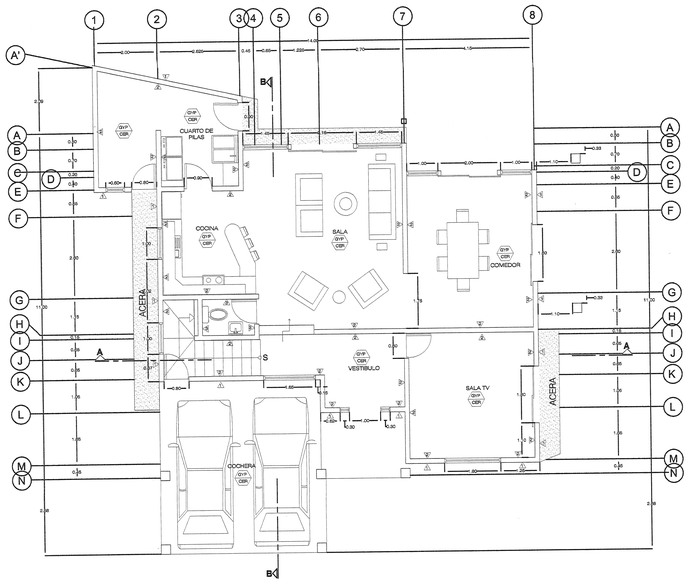

PLANTA ARQUITECTONICAS 1ER NIVEL
ESCALA 1:75

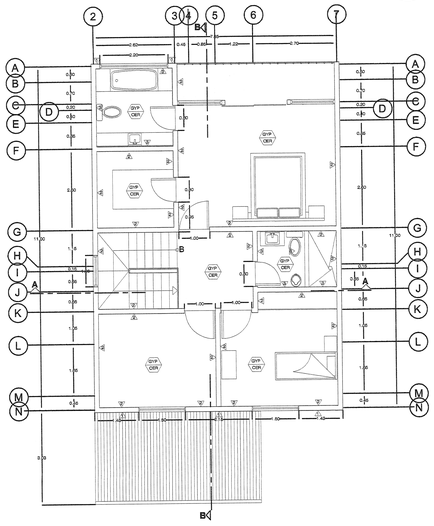

PLANTA ARQUITECTONICAS 2DO NIVEL
ESCALA 1:75


TABLA DE ACABADOS	
CIELOS	
GYP	CIELO EN GYPSUM
PISOS	
CER	PISO DE CERAMICA
AZU	PISO DE AZULEJO
PAREDES	
1	STUCCO COLOR GAMUZA
2	PINTURA ACRILICA BLANCO ISONO, DOS MANOS PARA INTERIORES
3	AZULEJO ALTURA GENERAL 1.20m Y 1.80m EN DUCHA O TINA

NOTA :


LAS PAREDES SERAN REPELLADAS, TIPO DE REPELLO QUEMADO Y EMPASTADO

COLOR, TEXTURA, MODELOS Y OTRO ASPECTOS ESTETICO ARQUITECTONICO A DEFINIR POR LA INSPECCION

SON COMPLEMENTARIAS A ESTAS "NOTAS GENERALES "LAS ESPECIFICACIONES TECNICAS DEL PROYECTO
EN CASO DE CONTRADICCIONES PREVALE LO QUE ESTABLEZCA LA INSPECCION DE LA OBRA

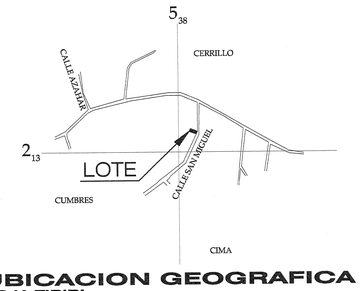


UBICACION GEOGRAFICA
HOJA TIRIBI
ESCALA 1:10000

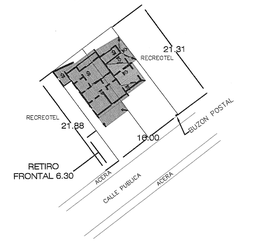


LOCALIZACION
ESCALA 1:500




ELEVACION FACHADA PRINCIPAL
ESCALA 1:50

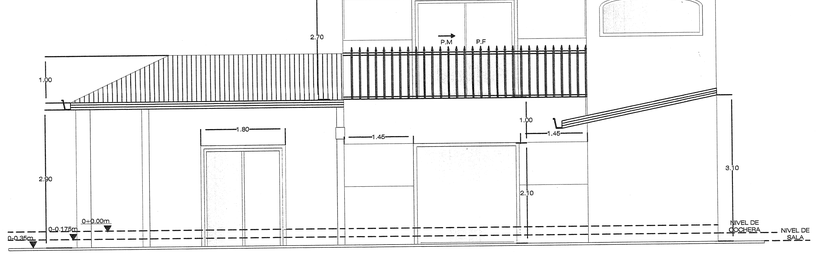

ELEVACION FACHADA POSTERIOR
ESCALA 1:50

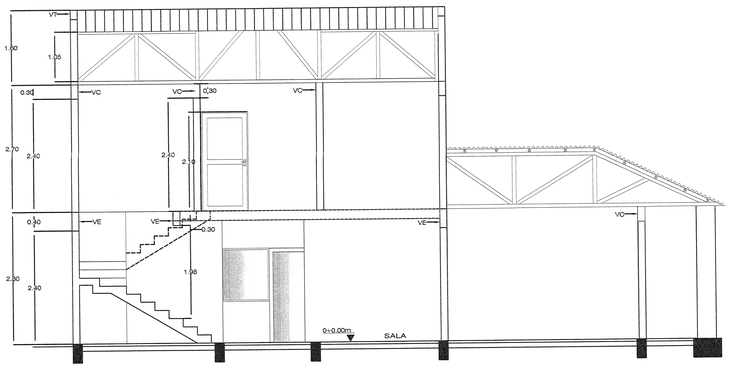

CORTE A-A
ESCALA 1:75

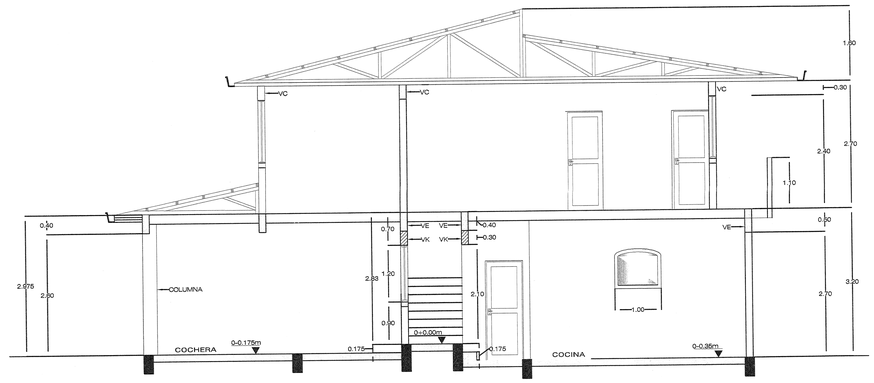

CORTE B-B
ESCALA 1:75

CFIA CFIA CFIA CFIA CFIA CFIA CFIA CFIA CFIA CFIA

COLEGIO FEDERADO DE INGENIEROS Y DE ARQUITECTOS DE COSTA RICA

Contrato OC-535355
Manto Tasado ¢52,520,000.00
Fecha: 06/04/2011
Catastro: C-853955-2003
Area tramitado: 221 m2
Profesional: IC-3129
Propietario: RECREOTEL S.A.

N° de Bitacora: P0093045
Factura: 1614095
Proyecto: CASA DE HABITACION. LOTE #2.

PROYECTO:
CASA DE HABITACION

PROPIETARIO:
RECREOTEL S.A

PROVINCIA	CANTON	DISTRITO
CARTAGO	LA UNION	SAN RAMON

DIBUJO:
ANGEL ROMAN S.

TERESITA CALVO QUESADA
IC-3129

PROFESIONAL RESPONSABLE DEL DISEÑO
NOMBRE: ING. TERESITA CALVO QUESADA
FIRMA Teresita Calvo Q. Nº: IC-3129

PROFESIONAL RESPONSABLE
DIRECCION TECNICA
NOMBRE: TERESITA CALVO QUESADA
FIRMA Teresita Calvo Q. Nº: IC-3129

INFORMACION REGISTRO PUBLICO
PROPIETARIO: RECREOTEL S.A
Nº CATASTRO: C-853954-2003 C-853955-2003
FOLIO REAL: 212708-000 176885-000

CONTENIDO:
- INDICADO

ESCALA	FECHA	LAMINA
INDICADA	ABRIL 2011	1/6